




Фасад 1-4

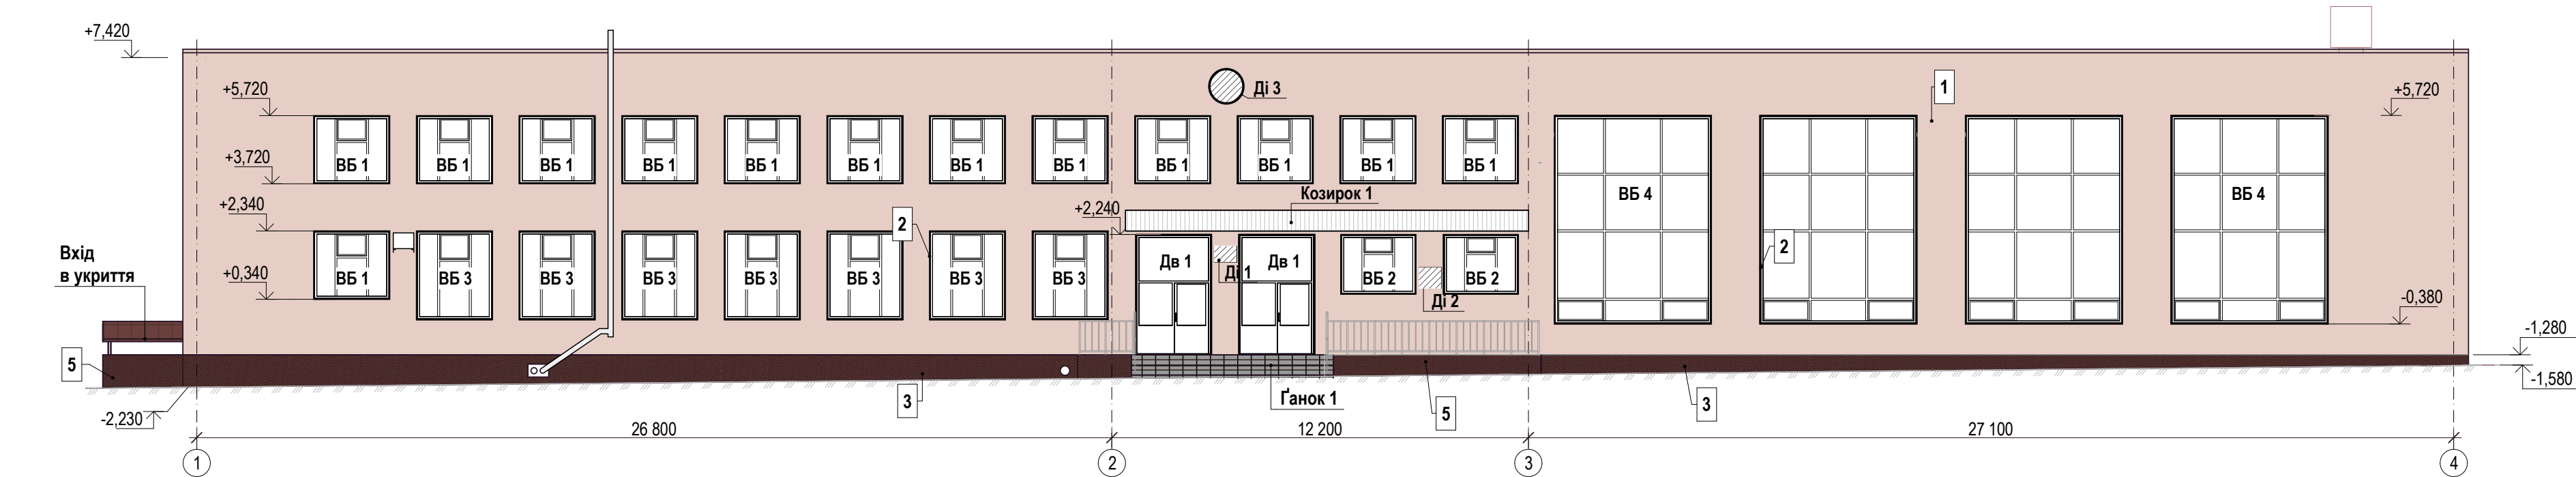

Фасад 4/1-1/1

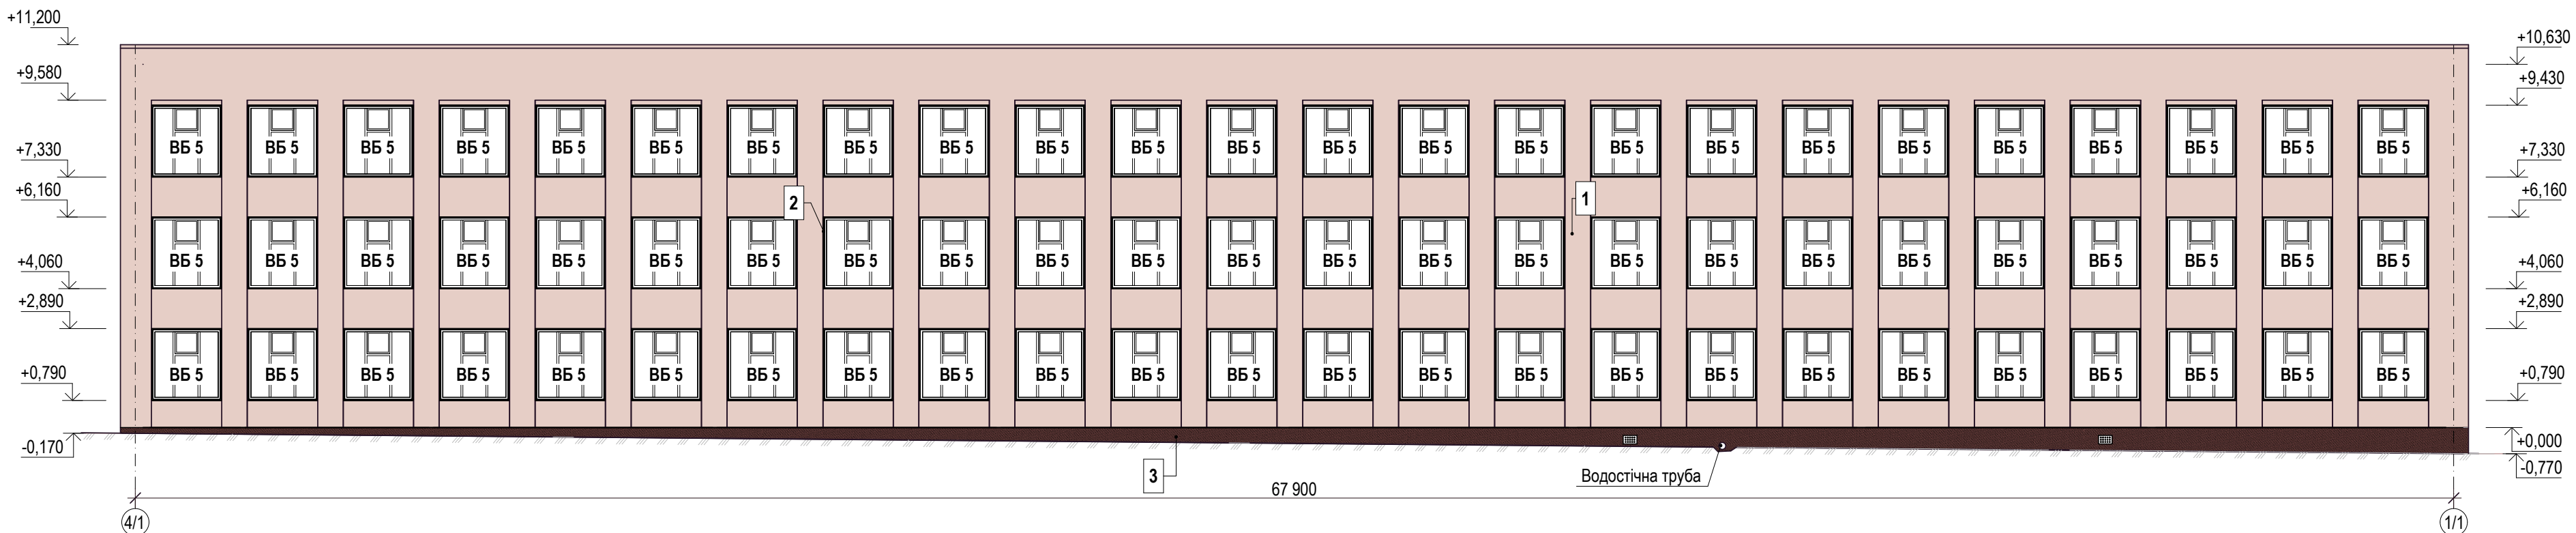

Фасад А-Г

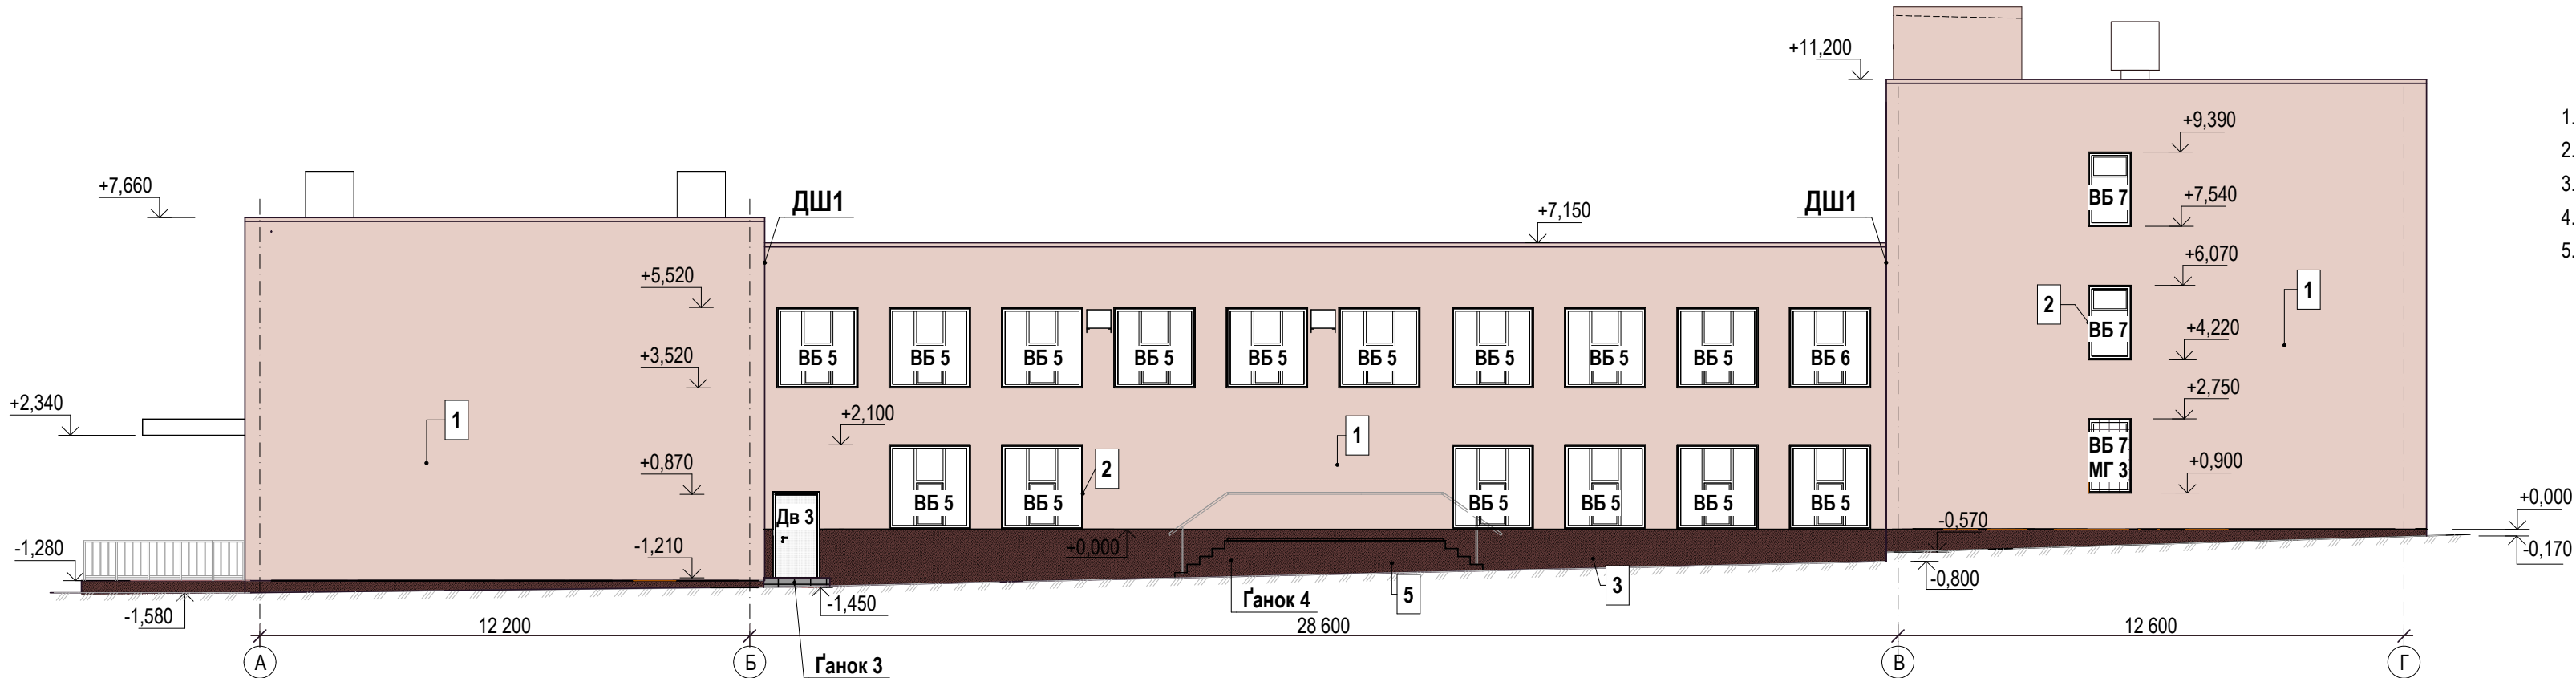

1. За відмітку 0,000 прийнято відмітку цоколю.
2. Вікна та двері, які незамарковано монтажу не підлягають.
3. Увага! Кольорову гаму фасаду виконати згідно завдання Замовника.
4. Фарбувати відкоси згідно кольору фасаду.
5. Відомість зовнішнього оздоблення див. 13.

Умовні позначення:

- ДШ - деформаційний шов
- 1 - тип опорядження

© ТОВ КЦП 2026р.

17262 - АБ

						17262 - АБ			
						Капітальний ремонт з часткової термомодернізації (заходи енергозбереження) Криворізького природничо-наукового ліцею Криворізької міської ради за адресою: вул. Володимира Великого, буд. 32а, м. Кривий Ріг, Дніпропетровська область			
Зм.	Кіл.	Лист	Недок.	Підпис	Дата				
Н.контроль	Кудряшов				03.26	Фасад 1-4, фасад 4/1-1/1, фасад А - Г.			
Перевірів	Темченко				03.26				
Виконав	Водоп'янова				03.26				
						ТОБ "Криворіжцивільпроект"			
						РП			
						11			
						Аркуші			
						Аркуші			

Формат А2